





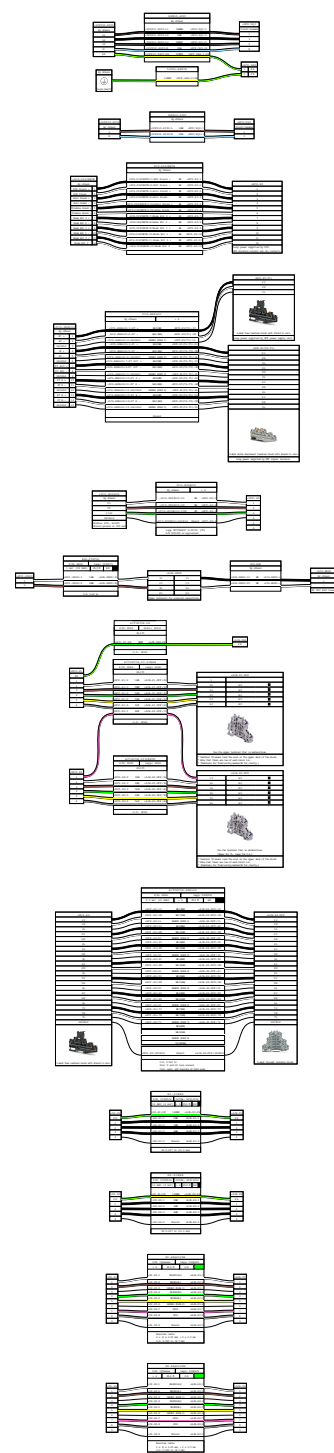


A								
REV	DESCRIPTION	ECN	DRAWN BY	CHECKED BY	APPROVED BY	DATE		
	MEI INC www.meaincorporated.com		TITLE: FIELD WIRING DRAWING					
			DWG NO. 10701622					REV. A0

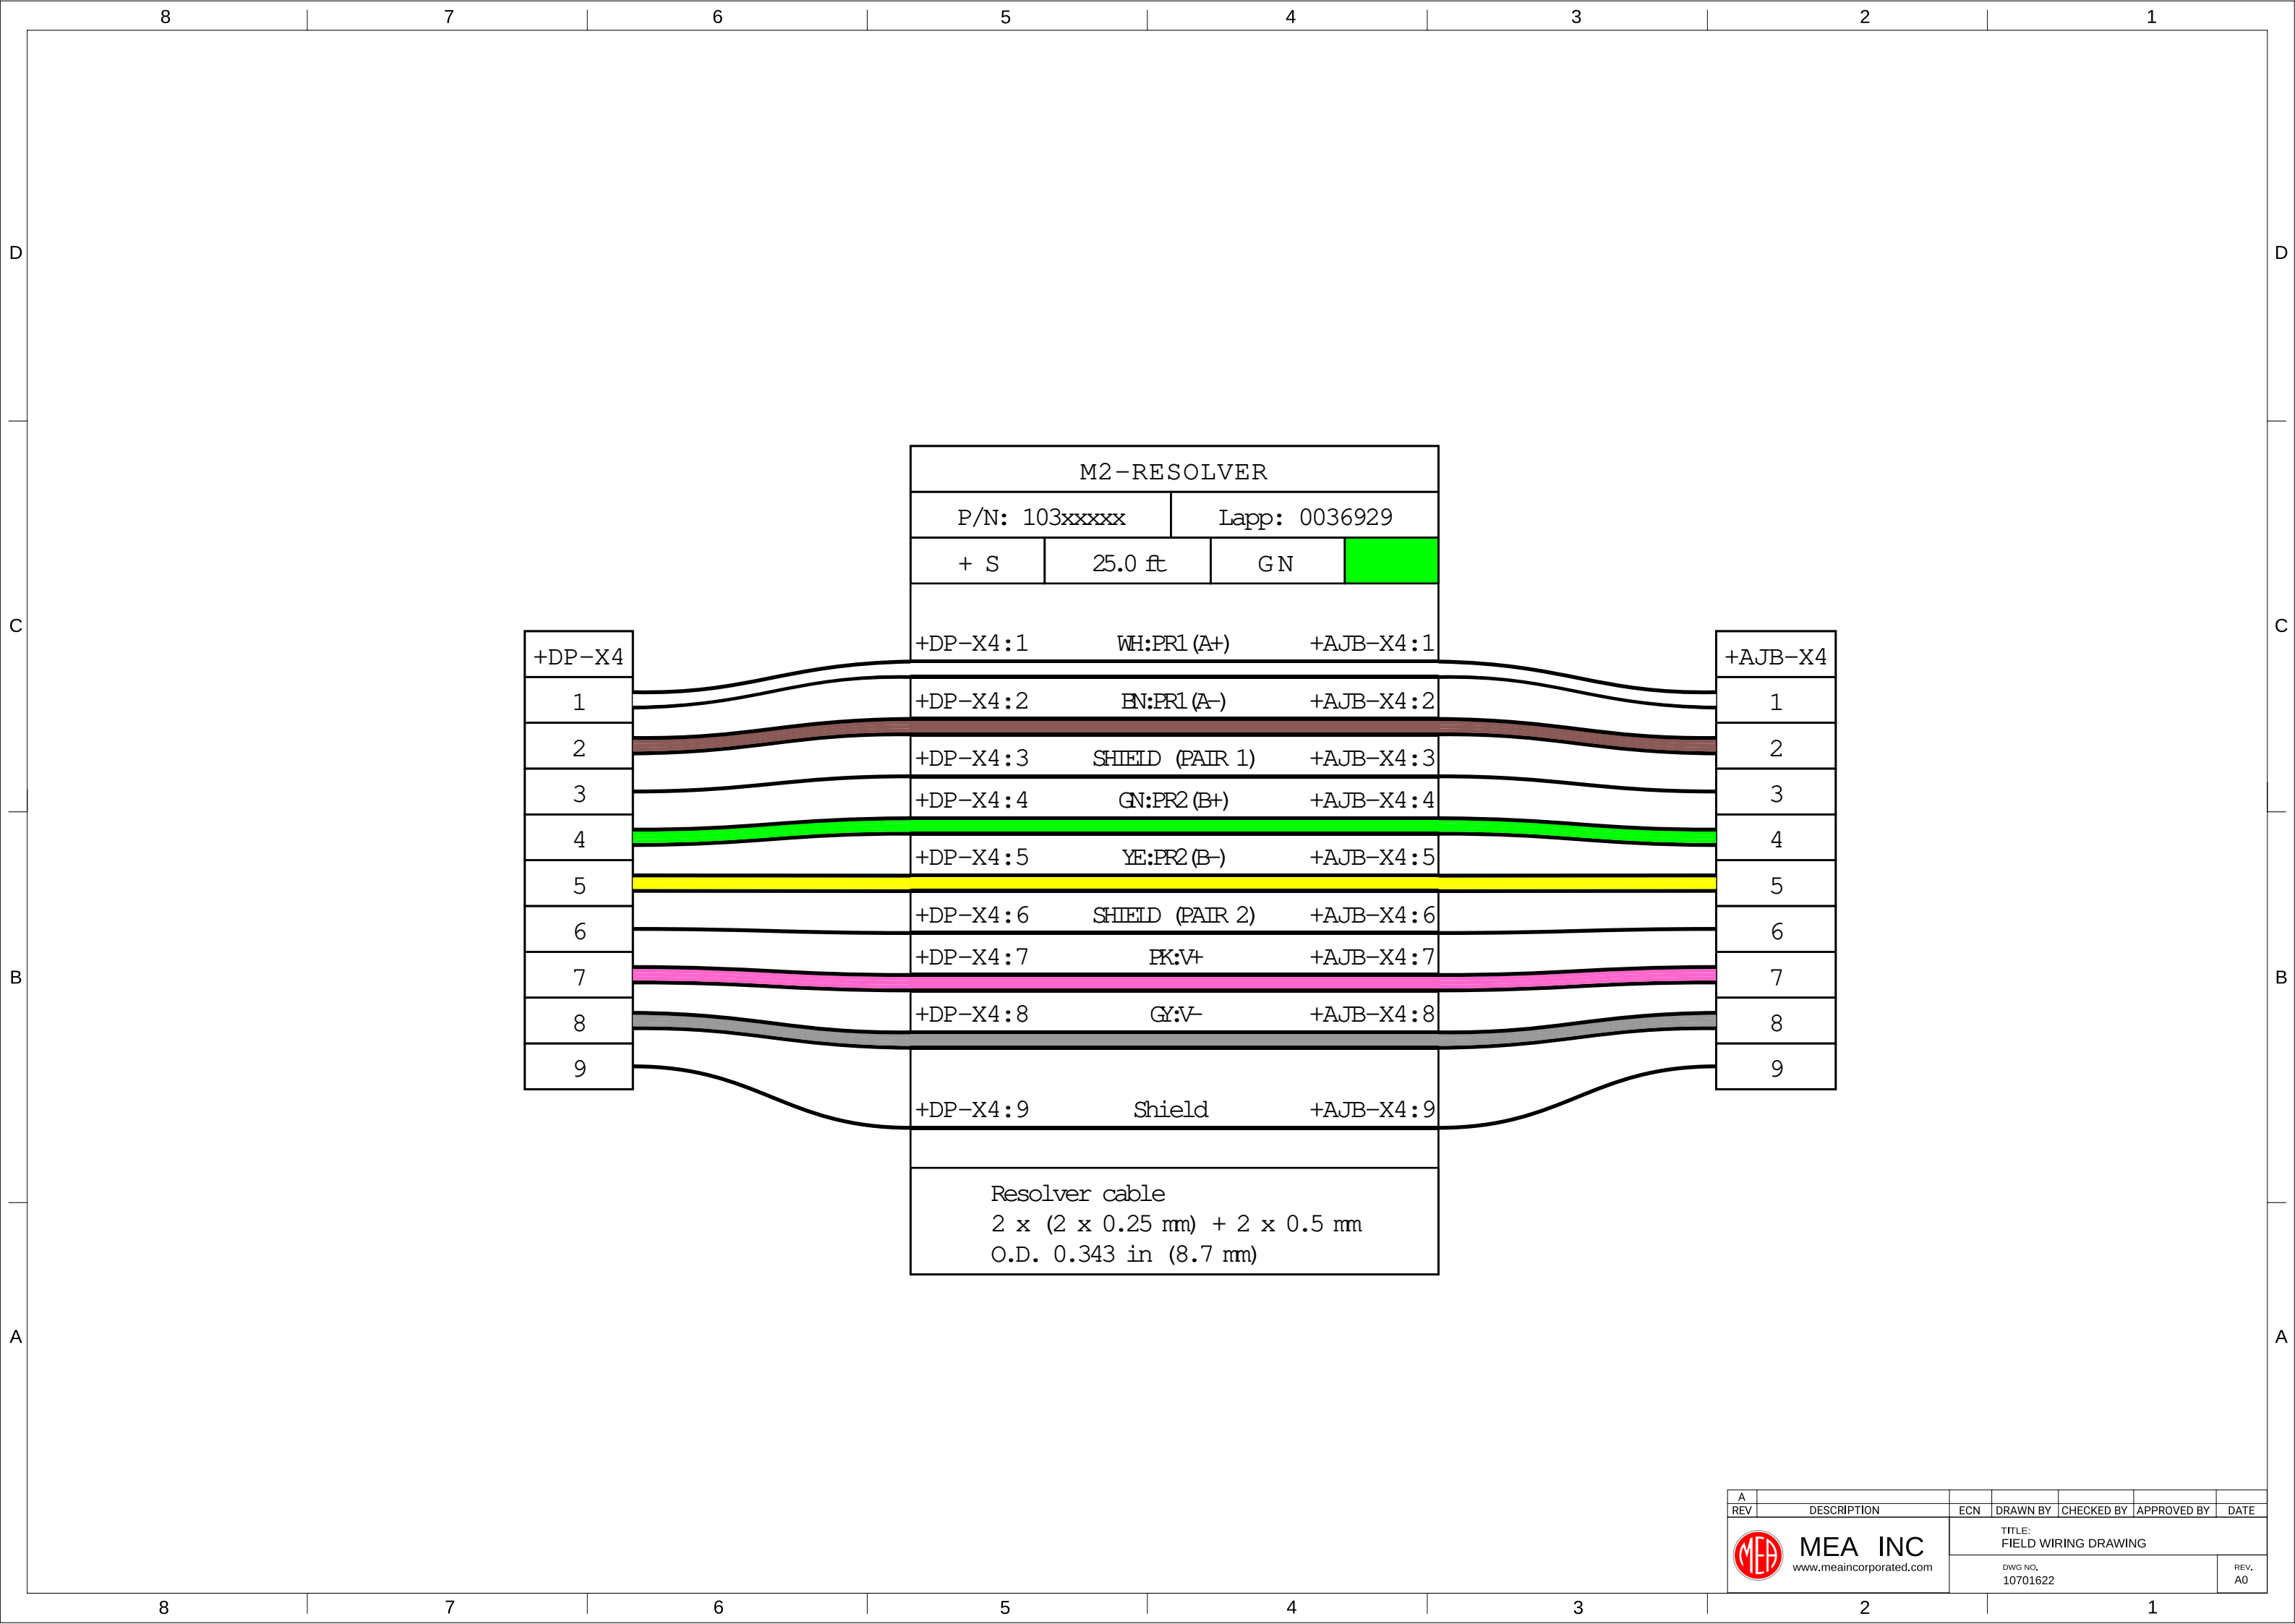

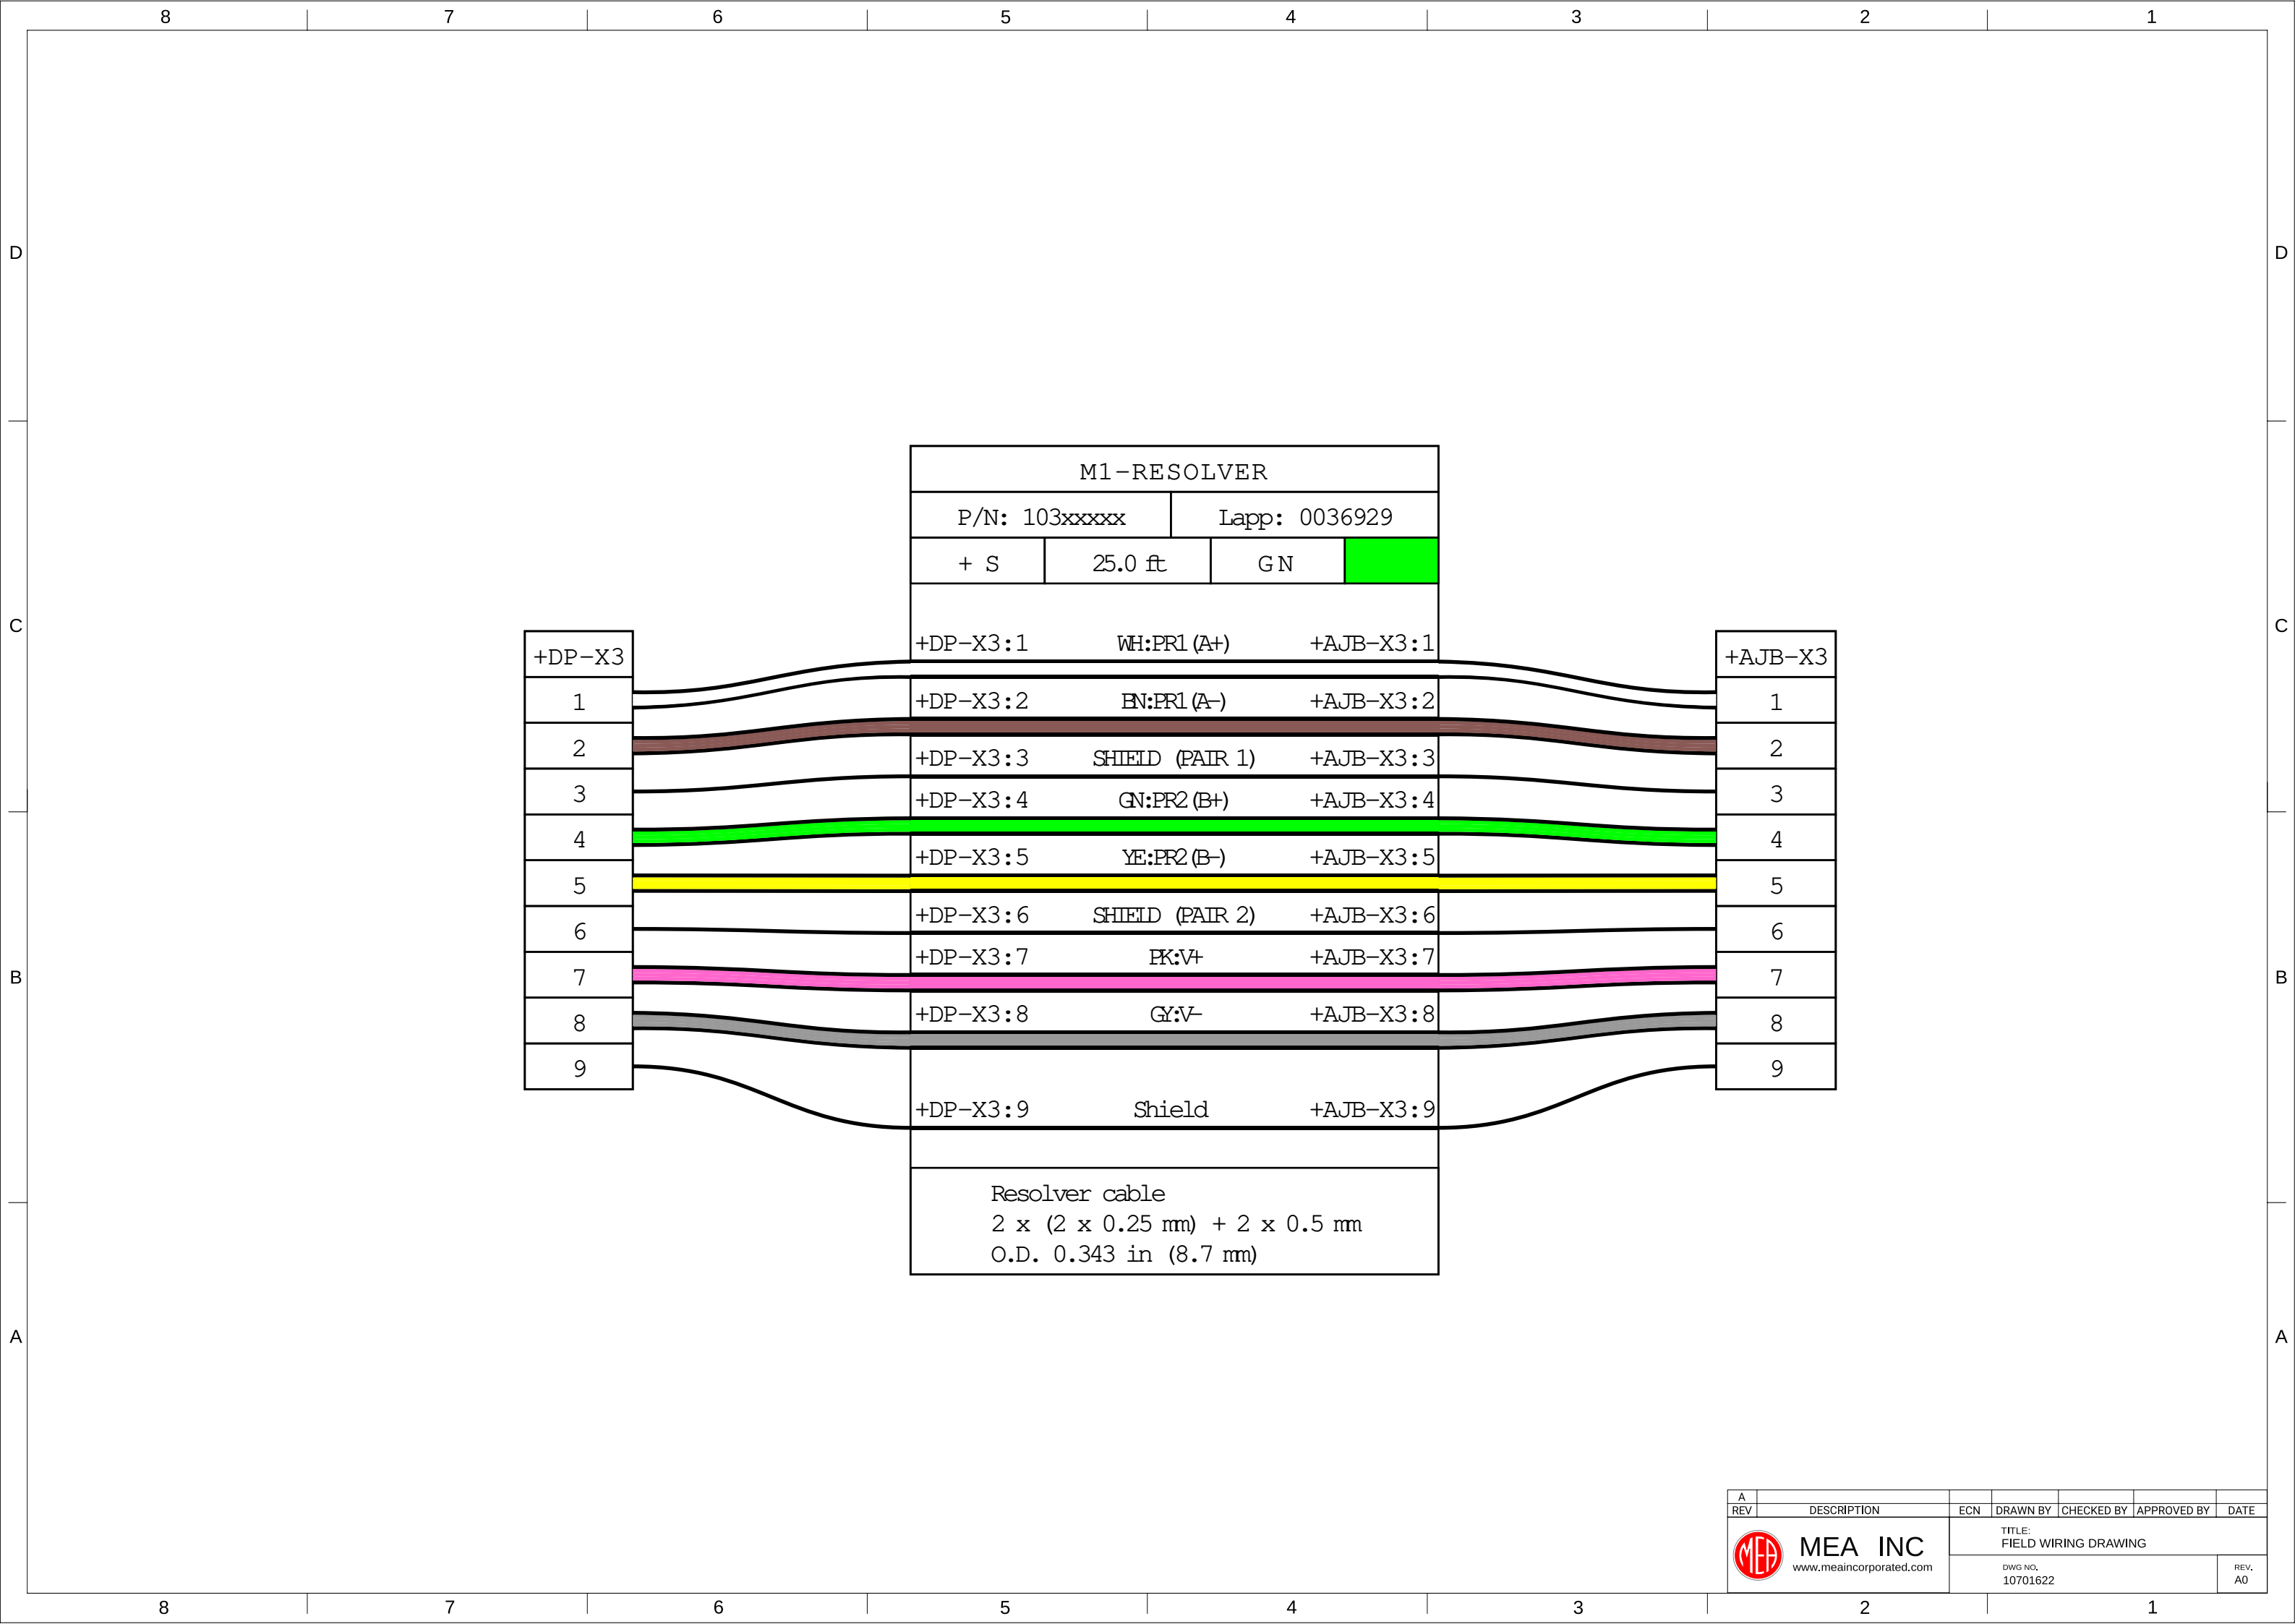

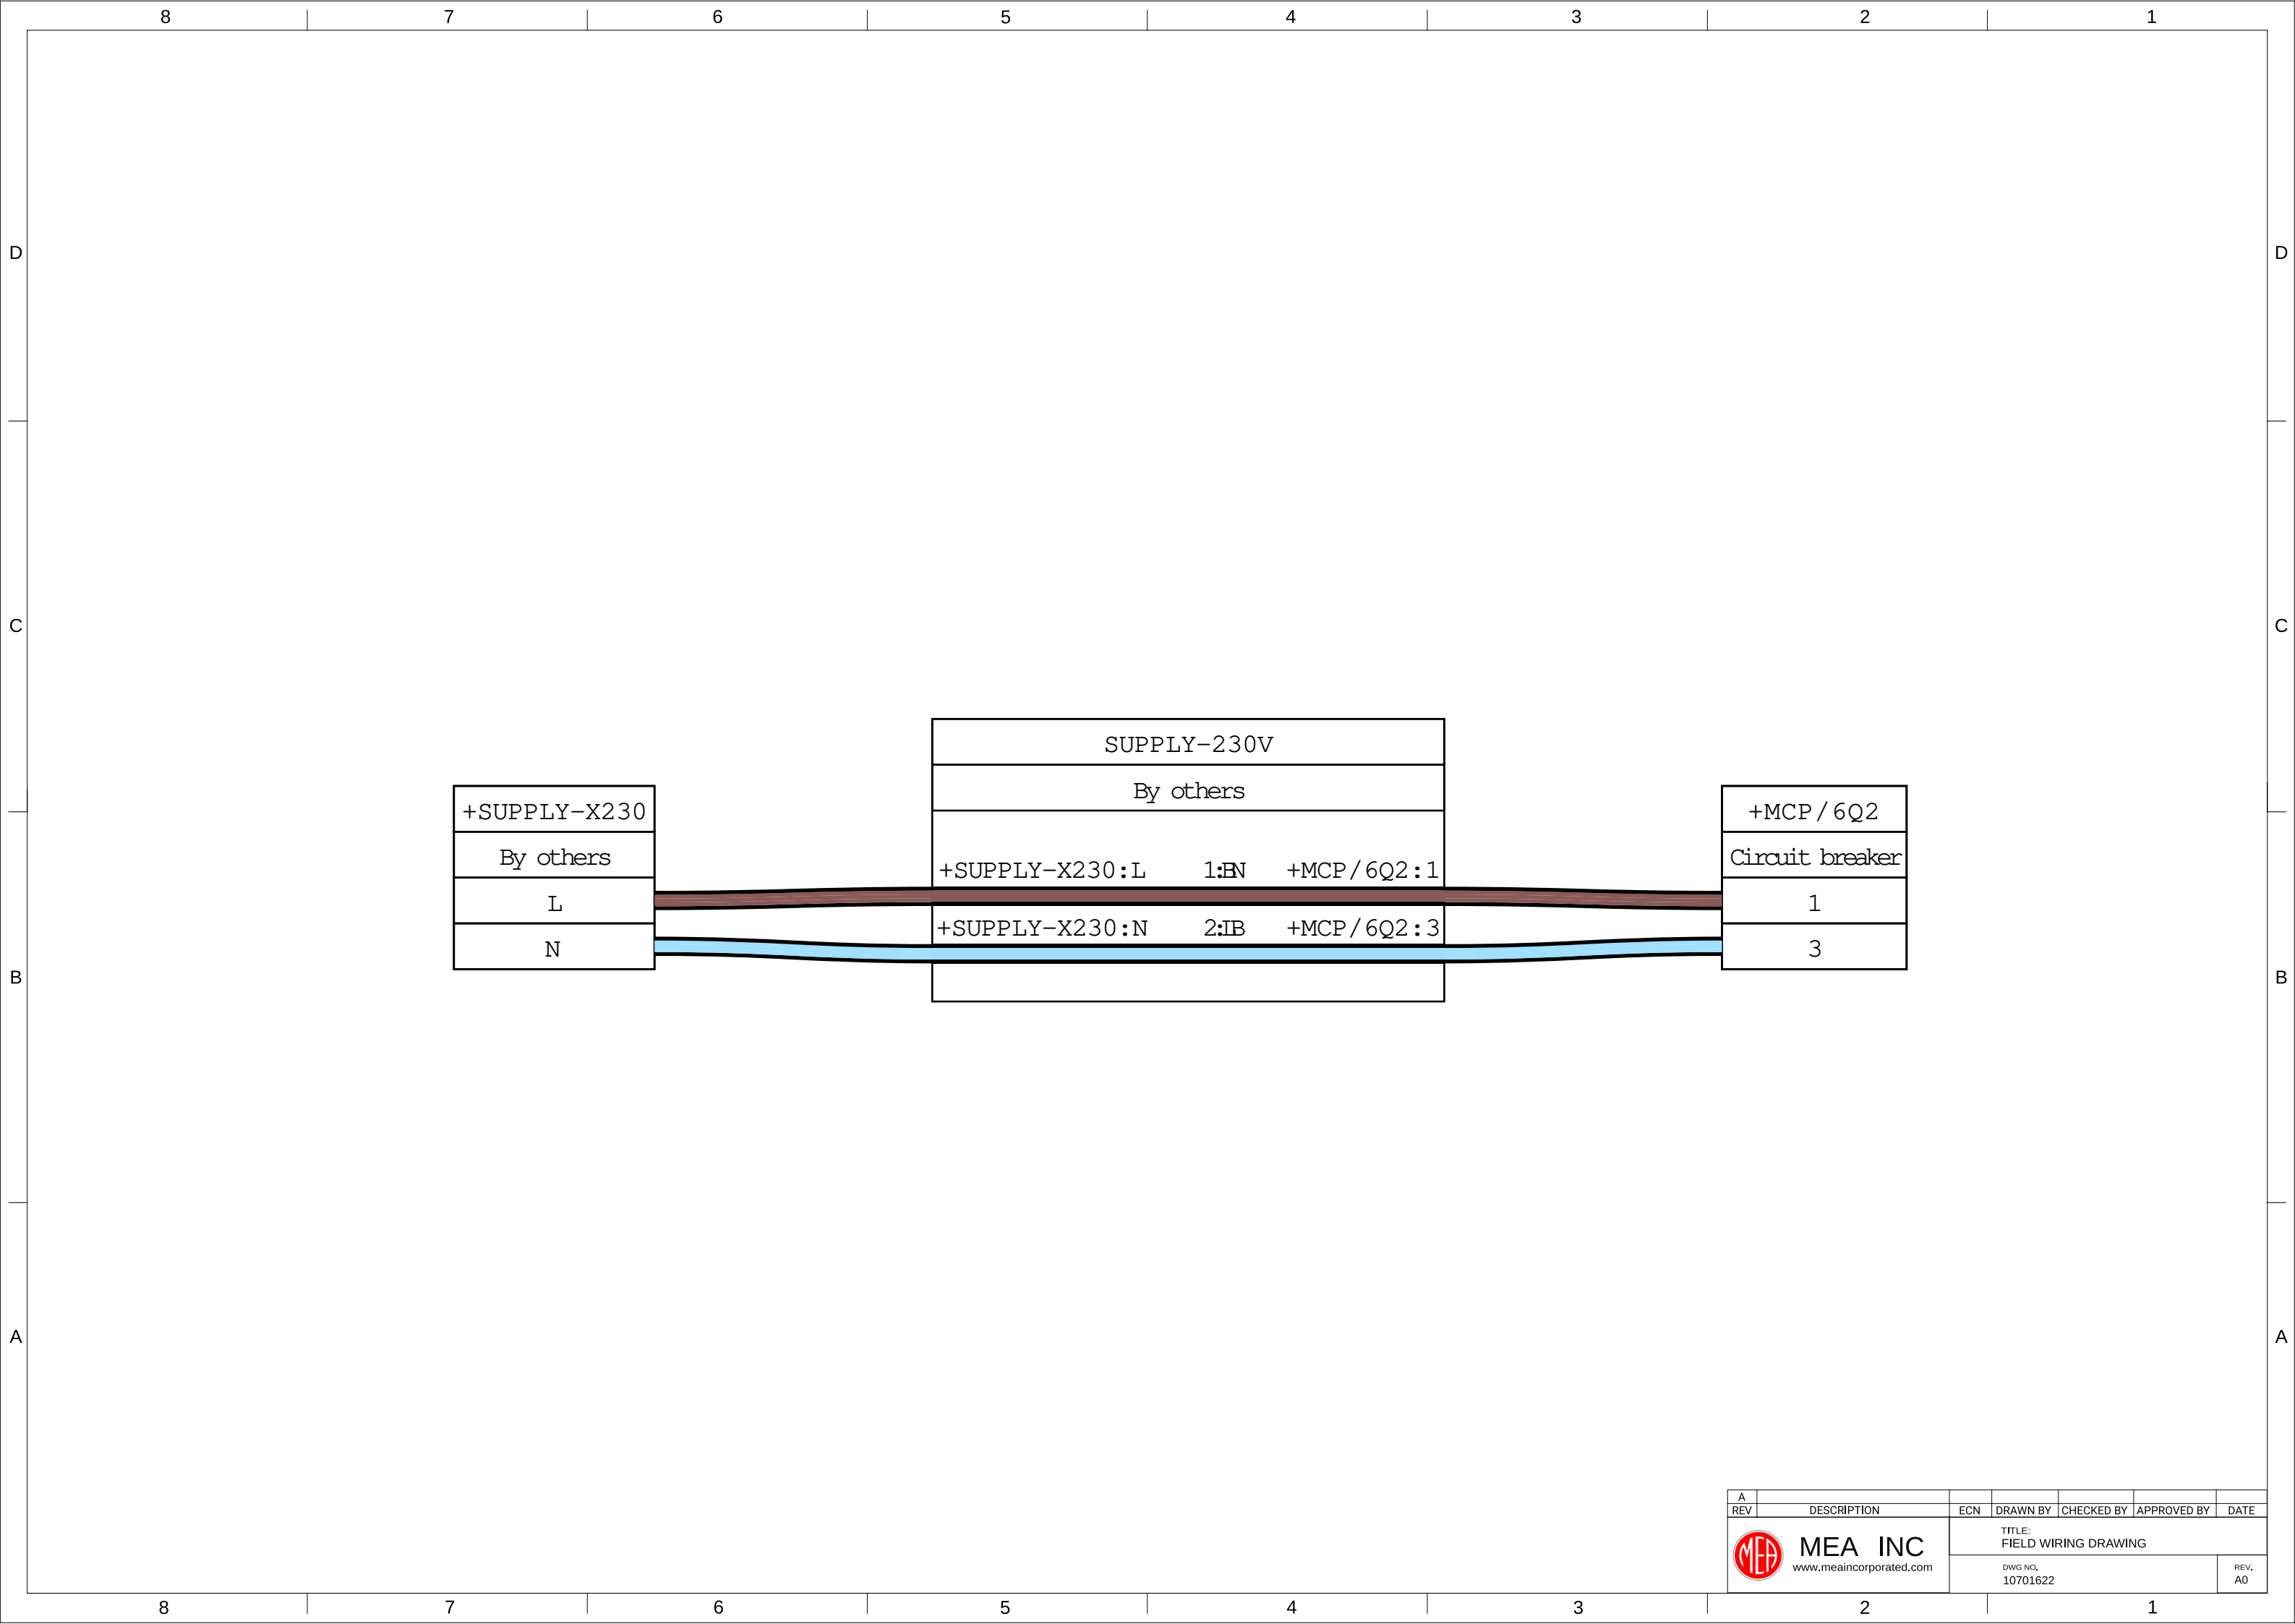

A						
REV	DESCRIPTION	ECN	DRAWN BY	CHECKED BY	APPROVED BY	DATE
 MEA INC www.meaincorporated.com		TITLE: FIELD WIRING DRAWING				
		DWG NO. 10701622				
					REV. A0	

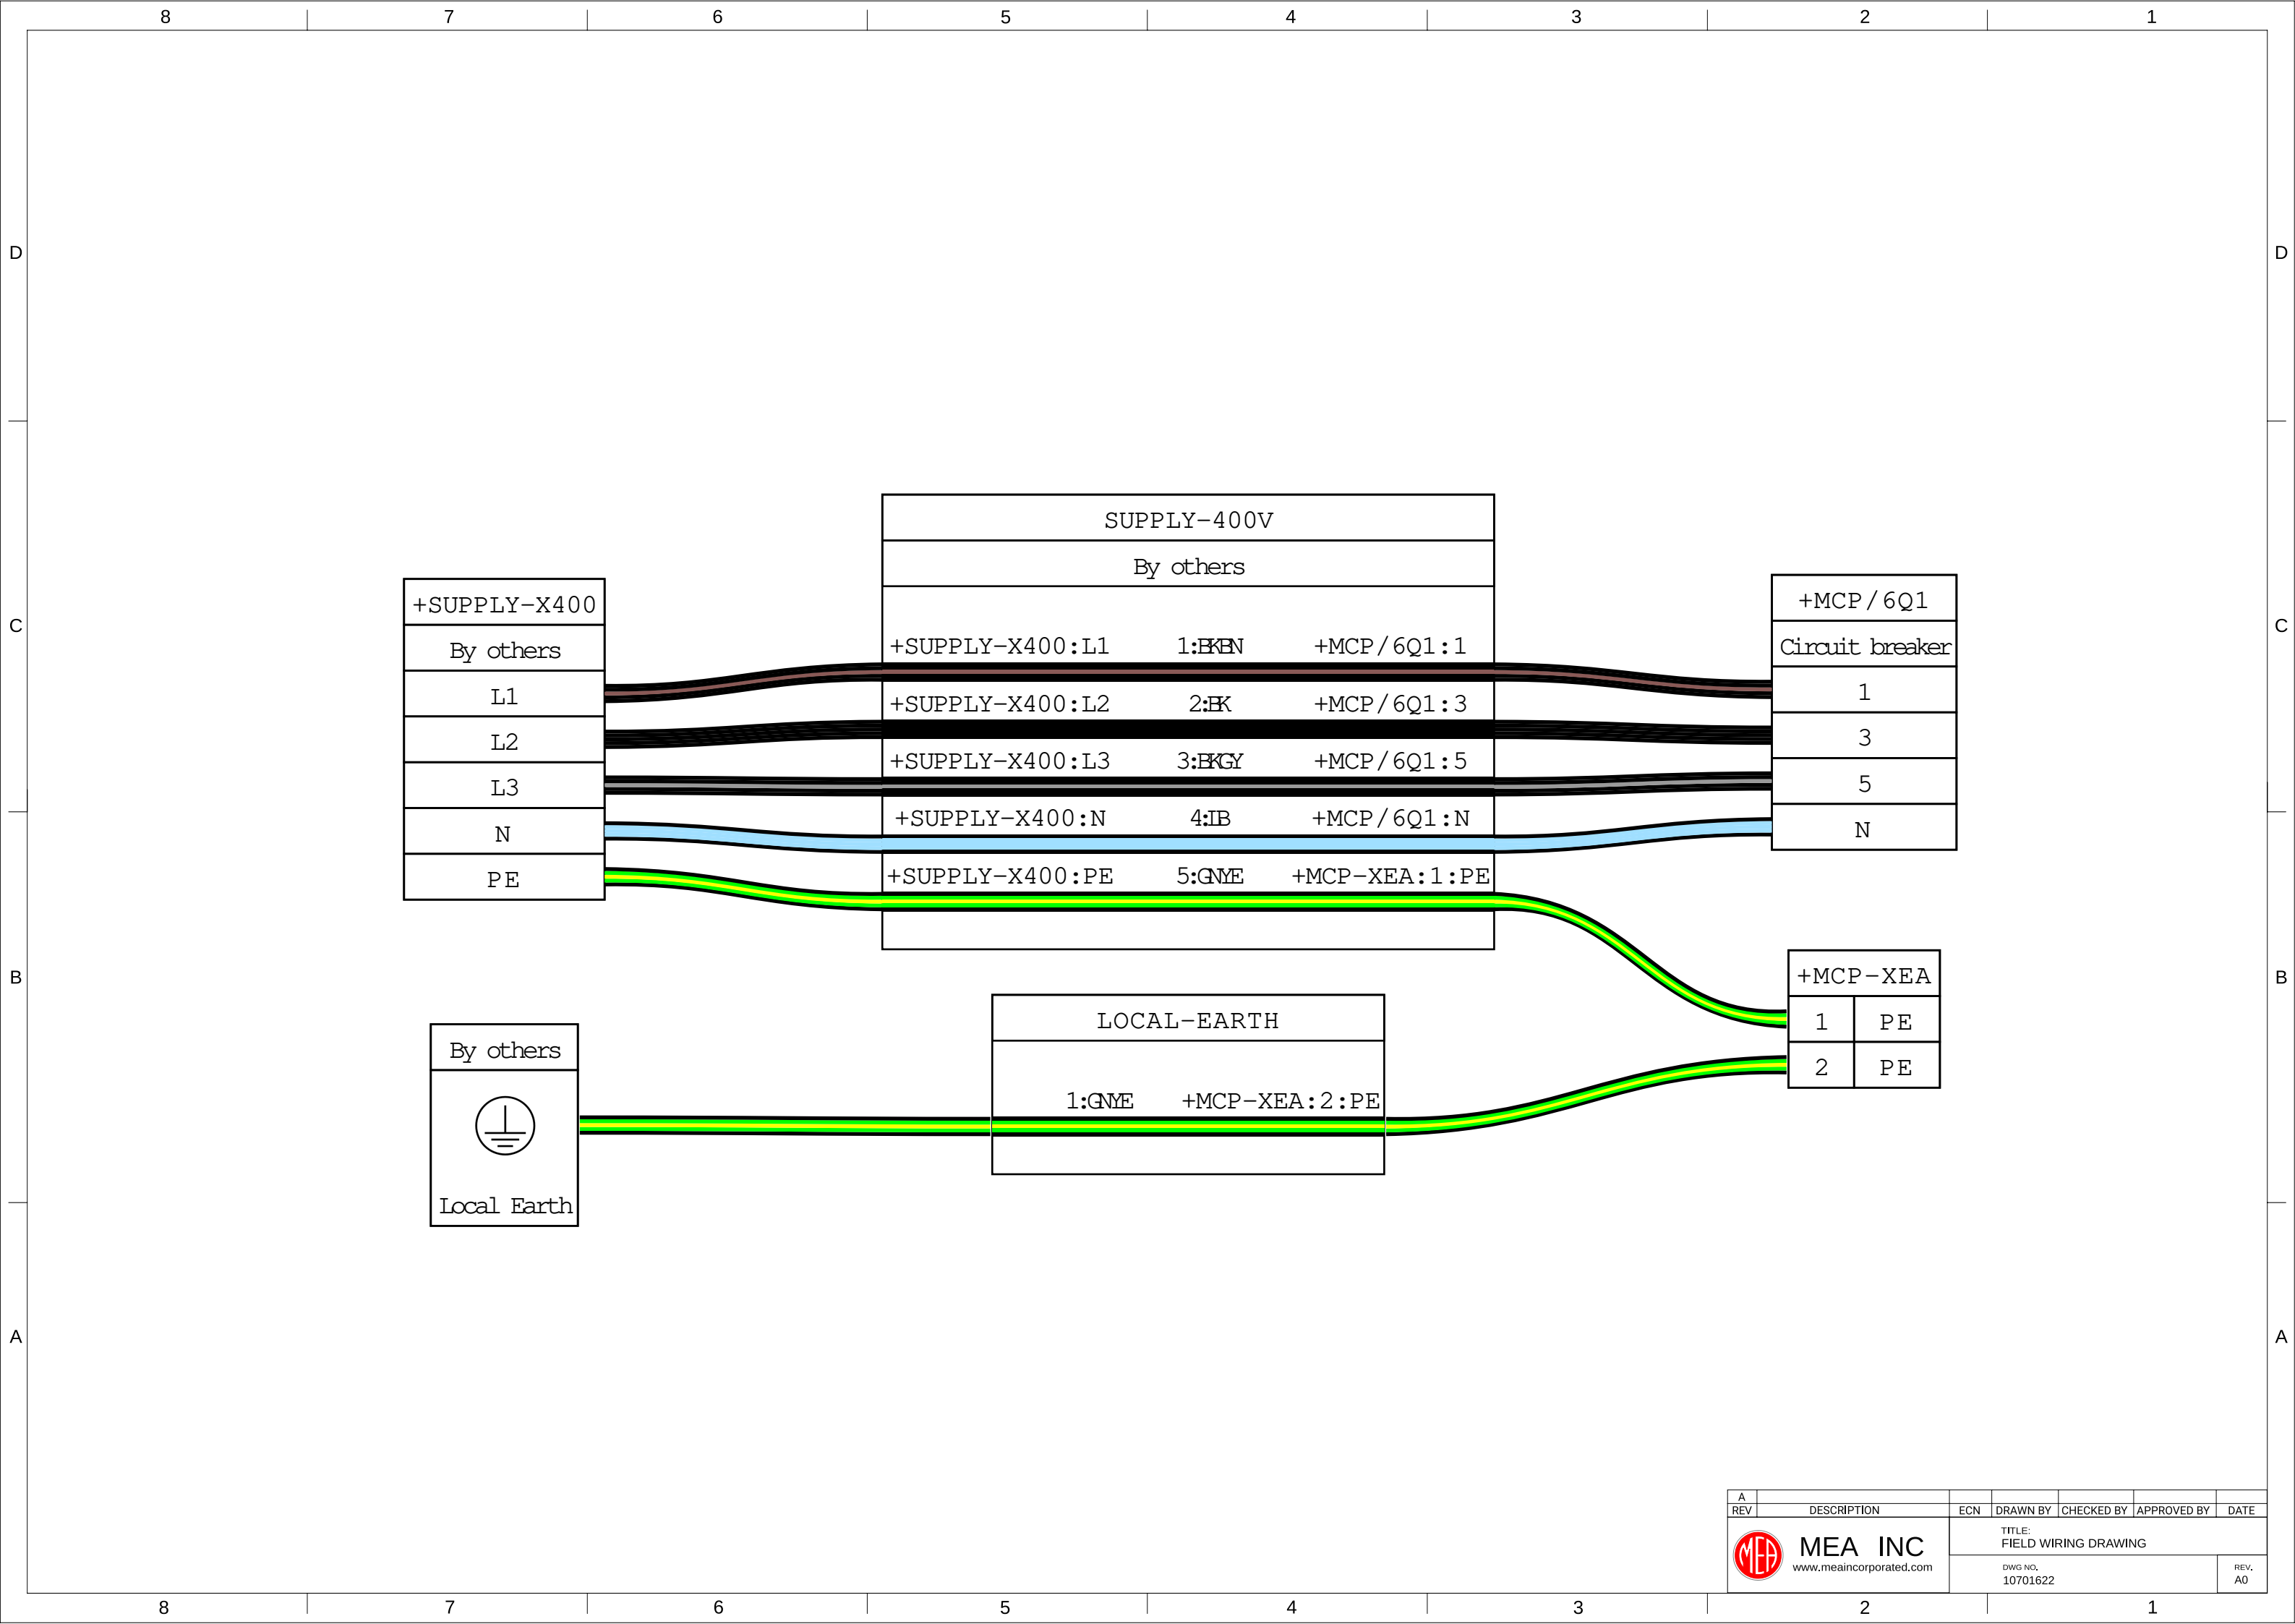

D

D

C


C

B


B

A


A

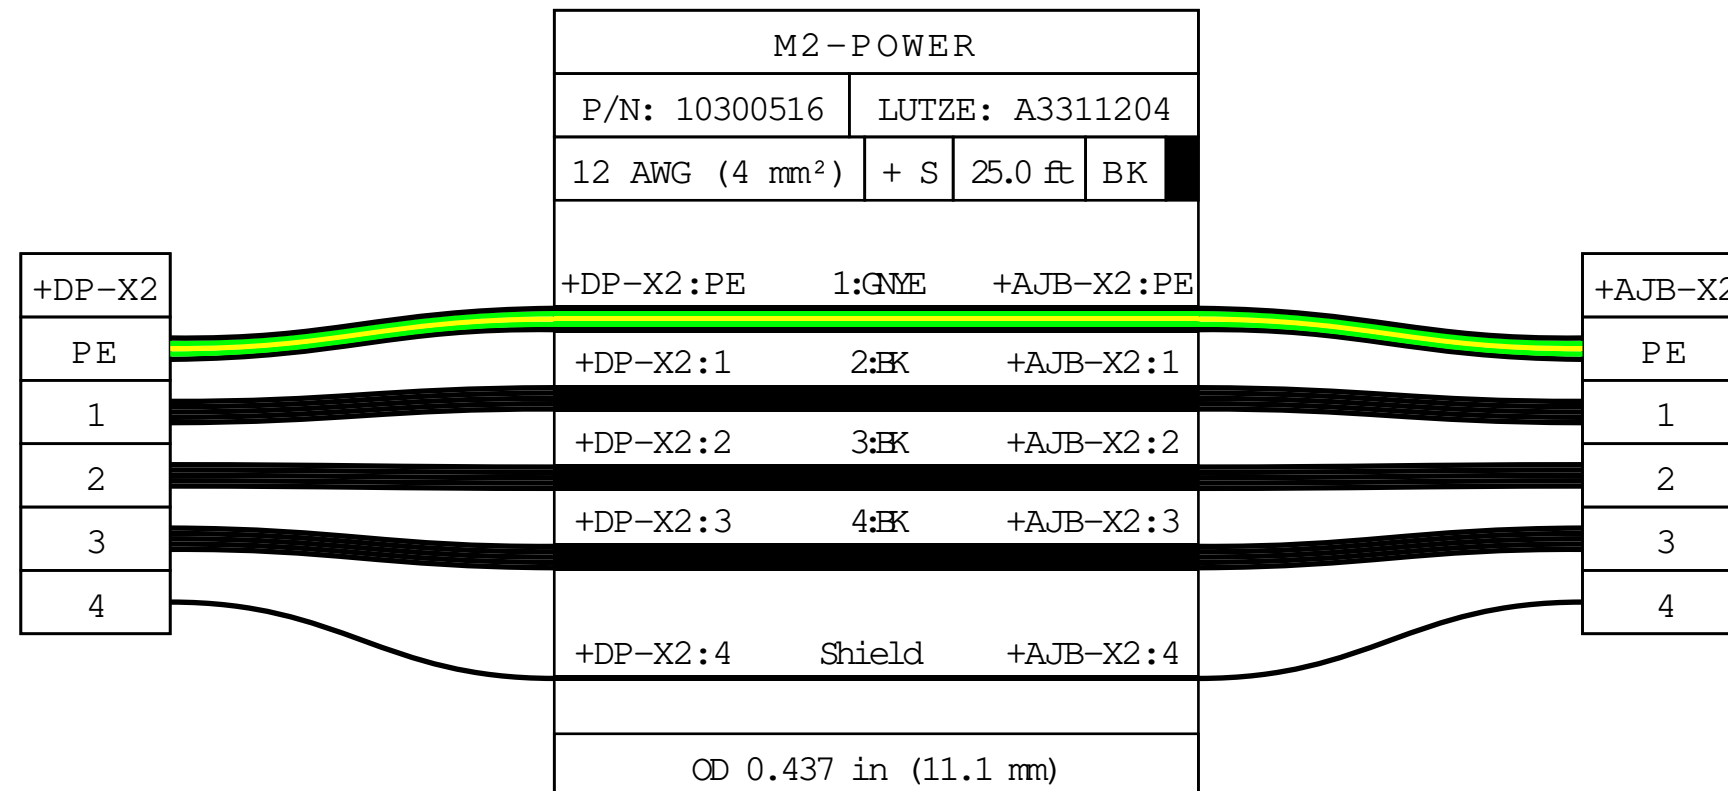



A REV	DESCRIPTION	ECN	DRAWN BY	CHECKED BY	APPROVED BY	DATE
	MEA INC www.meaincorporated.com	TITLE: FIELD WIRING DRAWING				
		DWG NO. 10701622				REV. A0

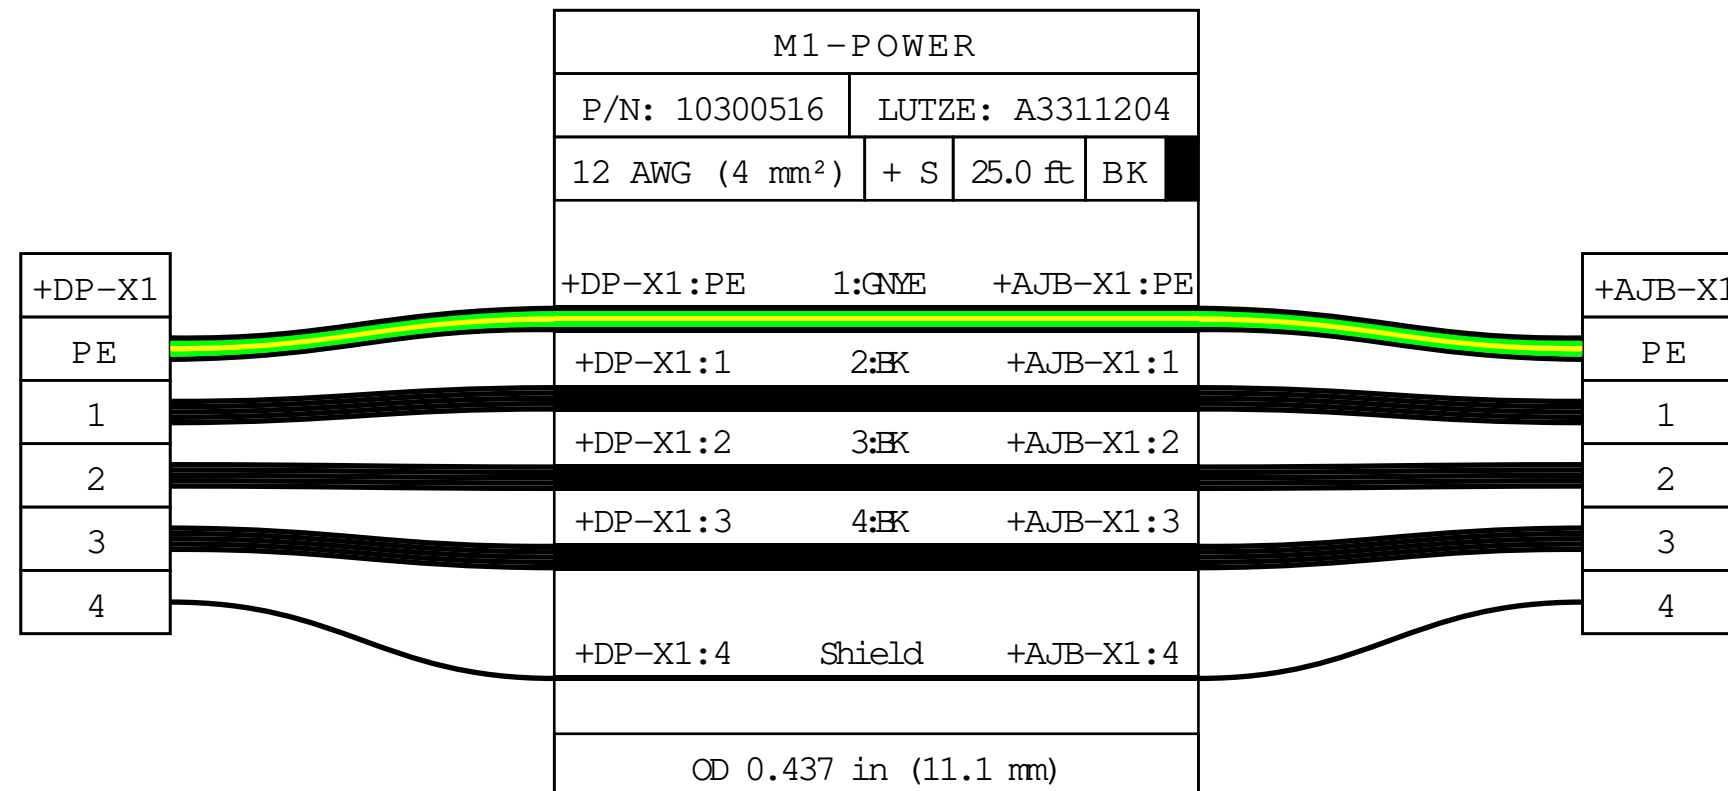

A REV	DESCRIPTION	ECN	DRAWN BY	CHECKED BY	APPROVED BY	DATE
	MEA INC www.meaincorporated.com	TITLE: FIELD WIRING DRAWING				
		DWG NO. 10701622				REV. A0

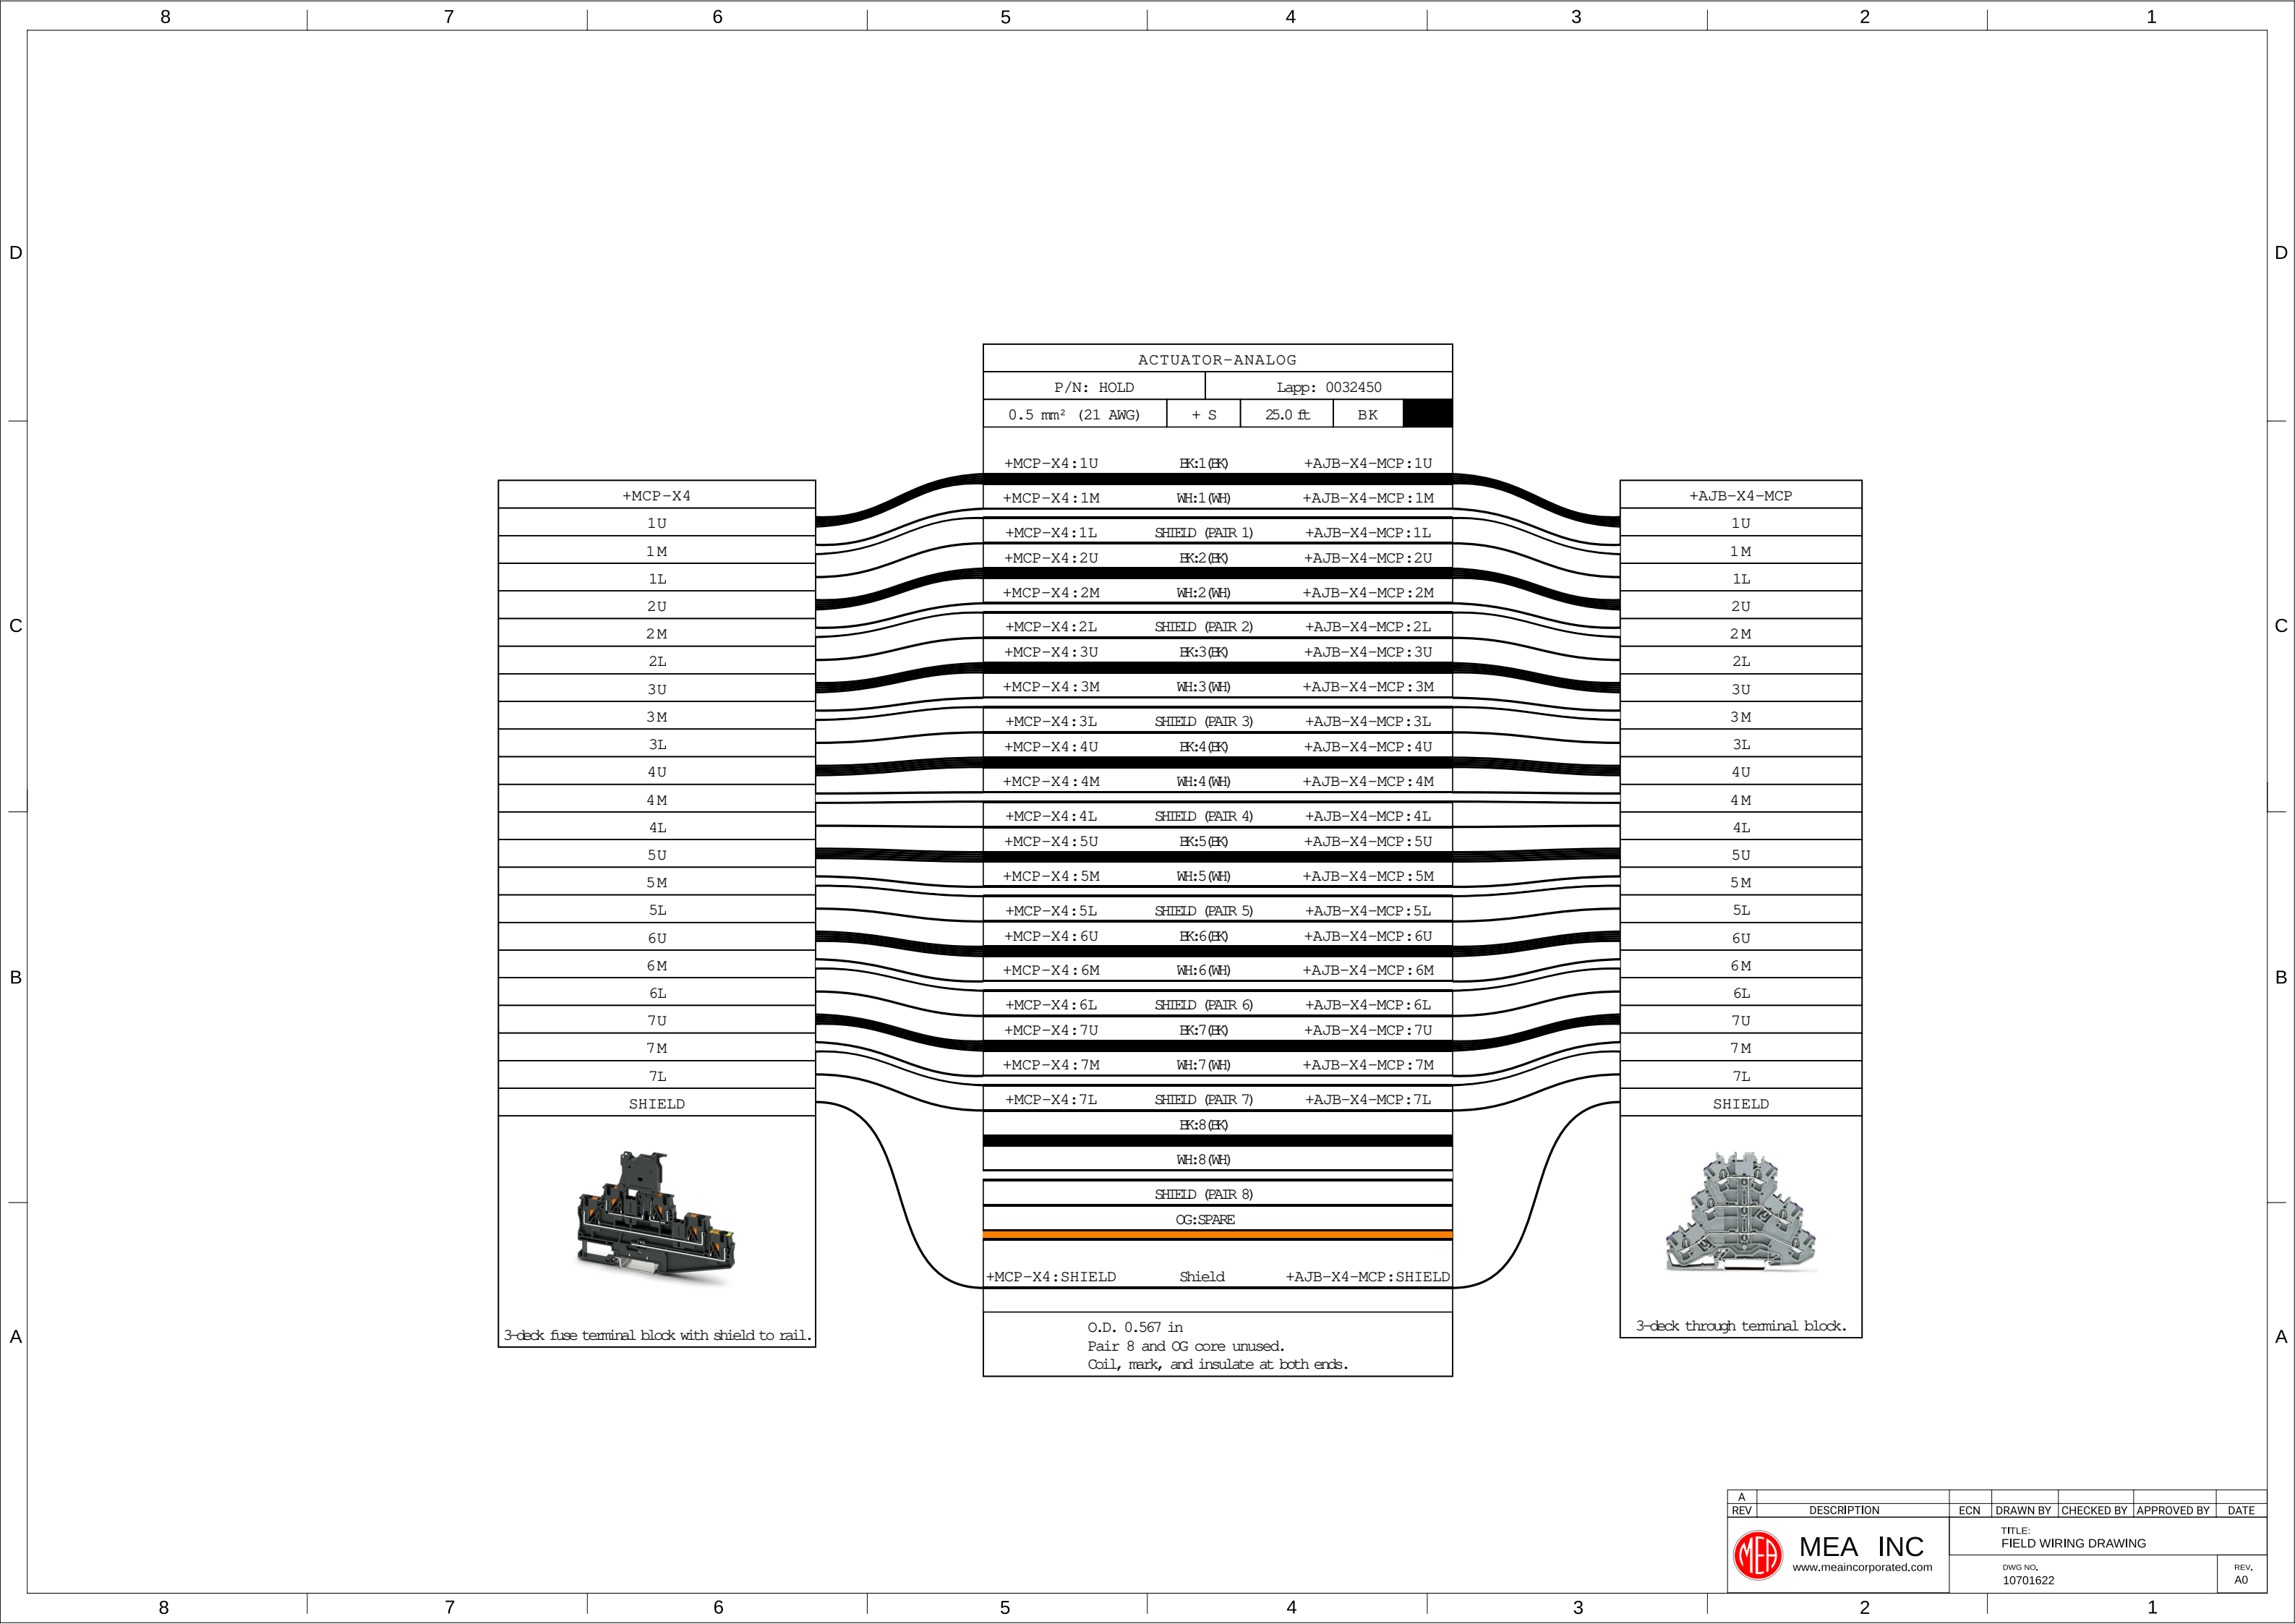

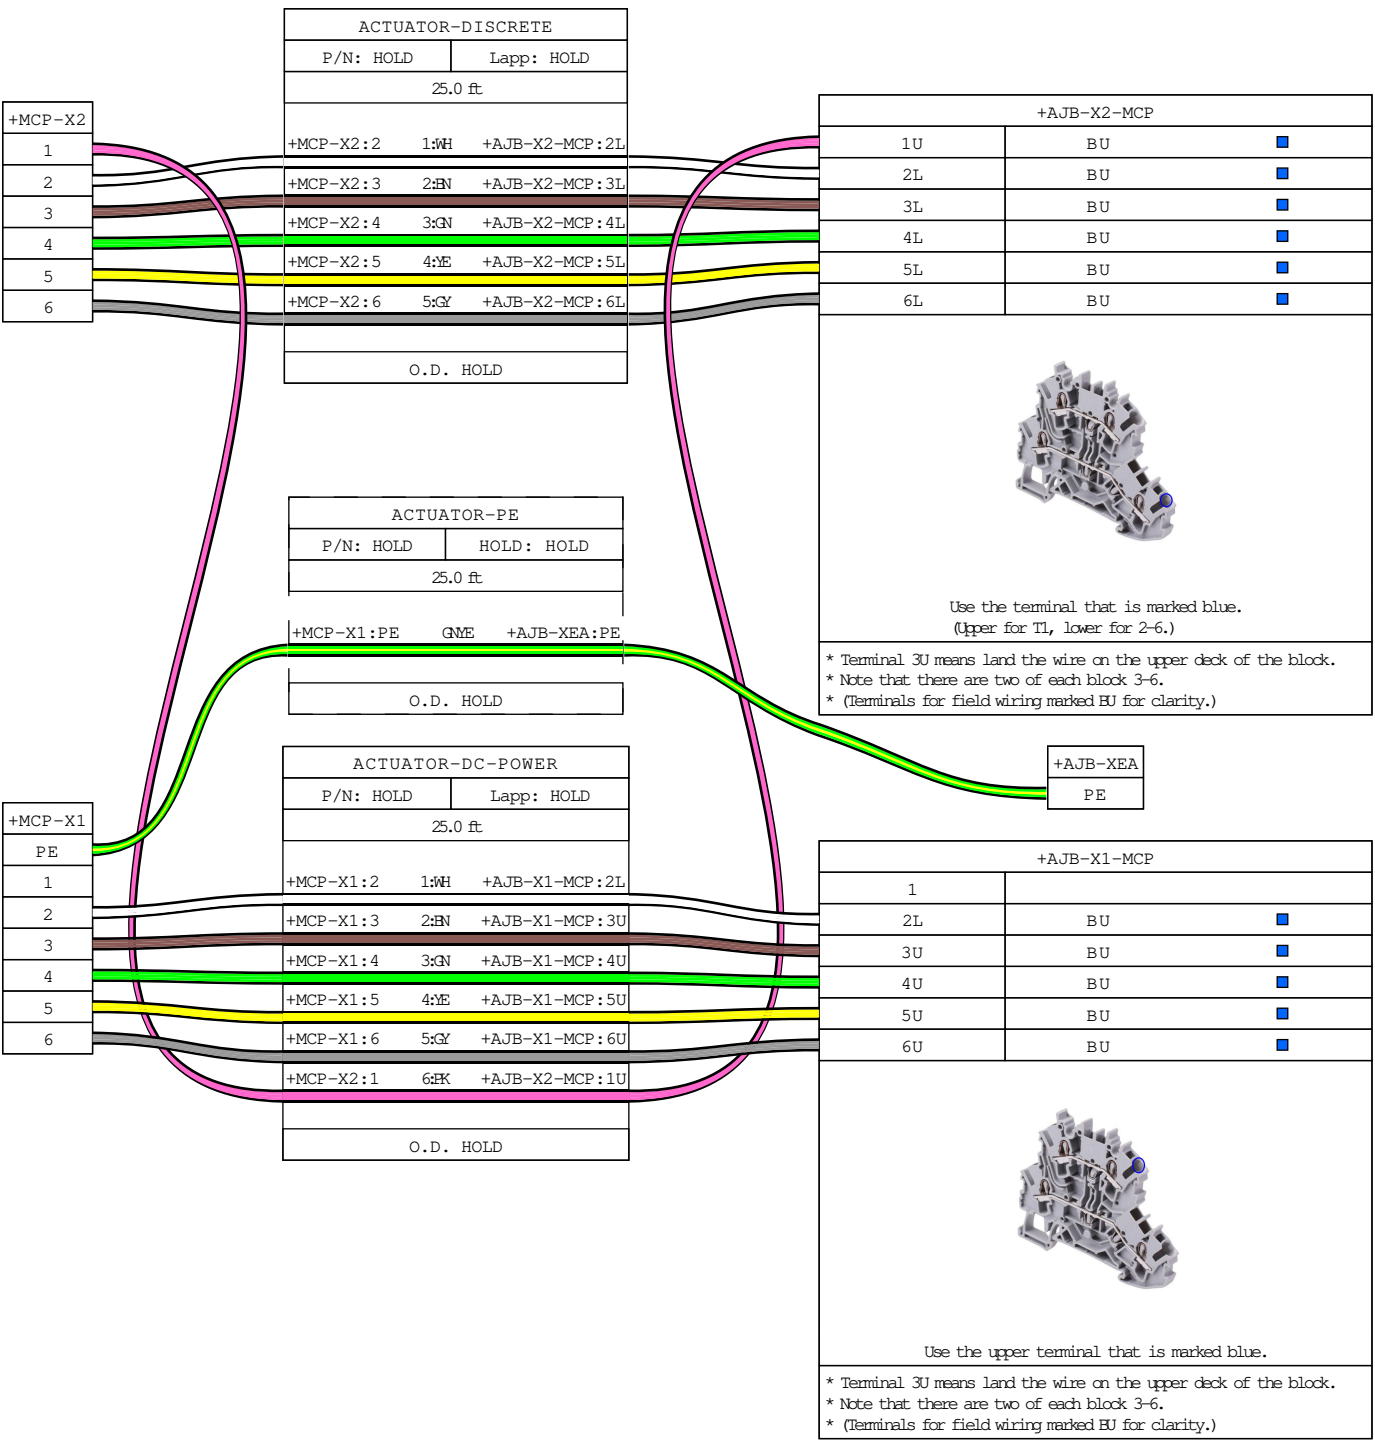

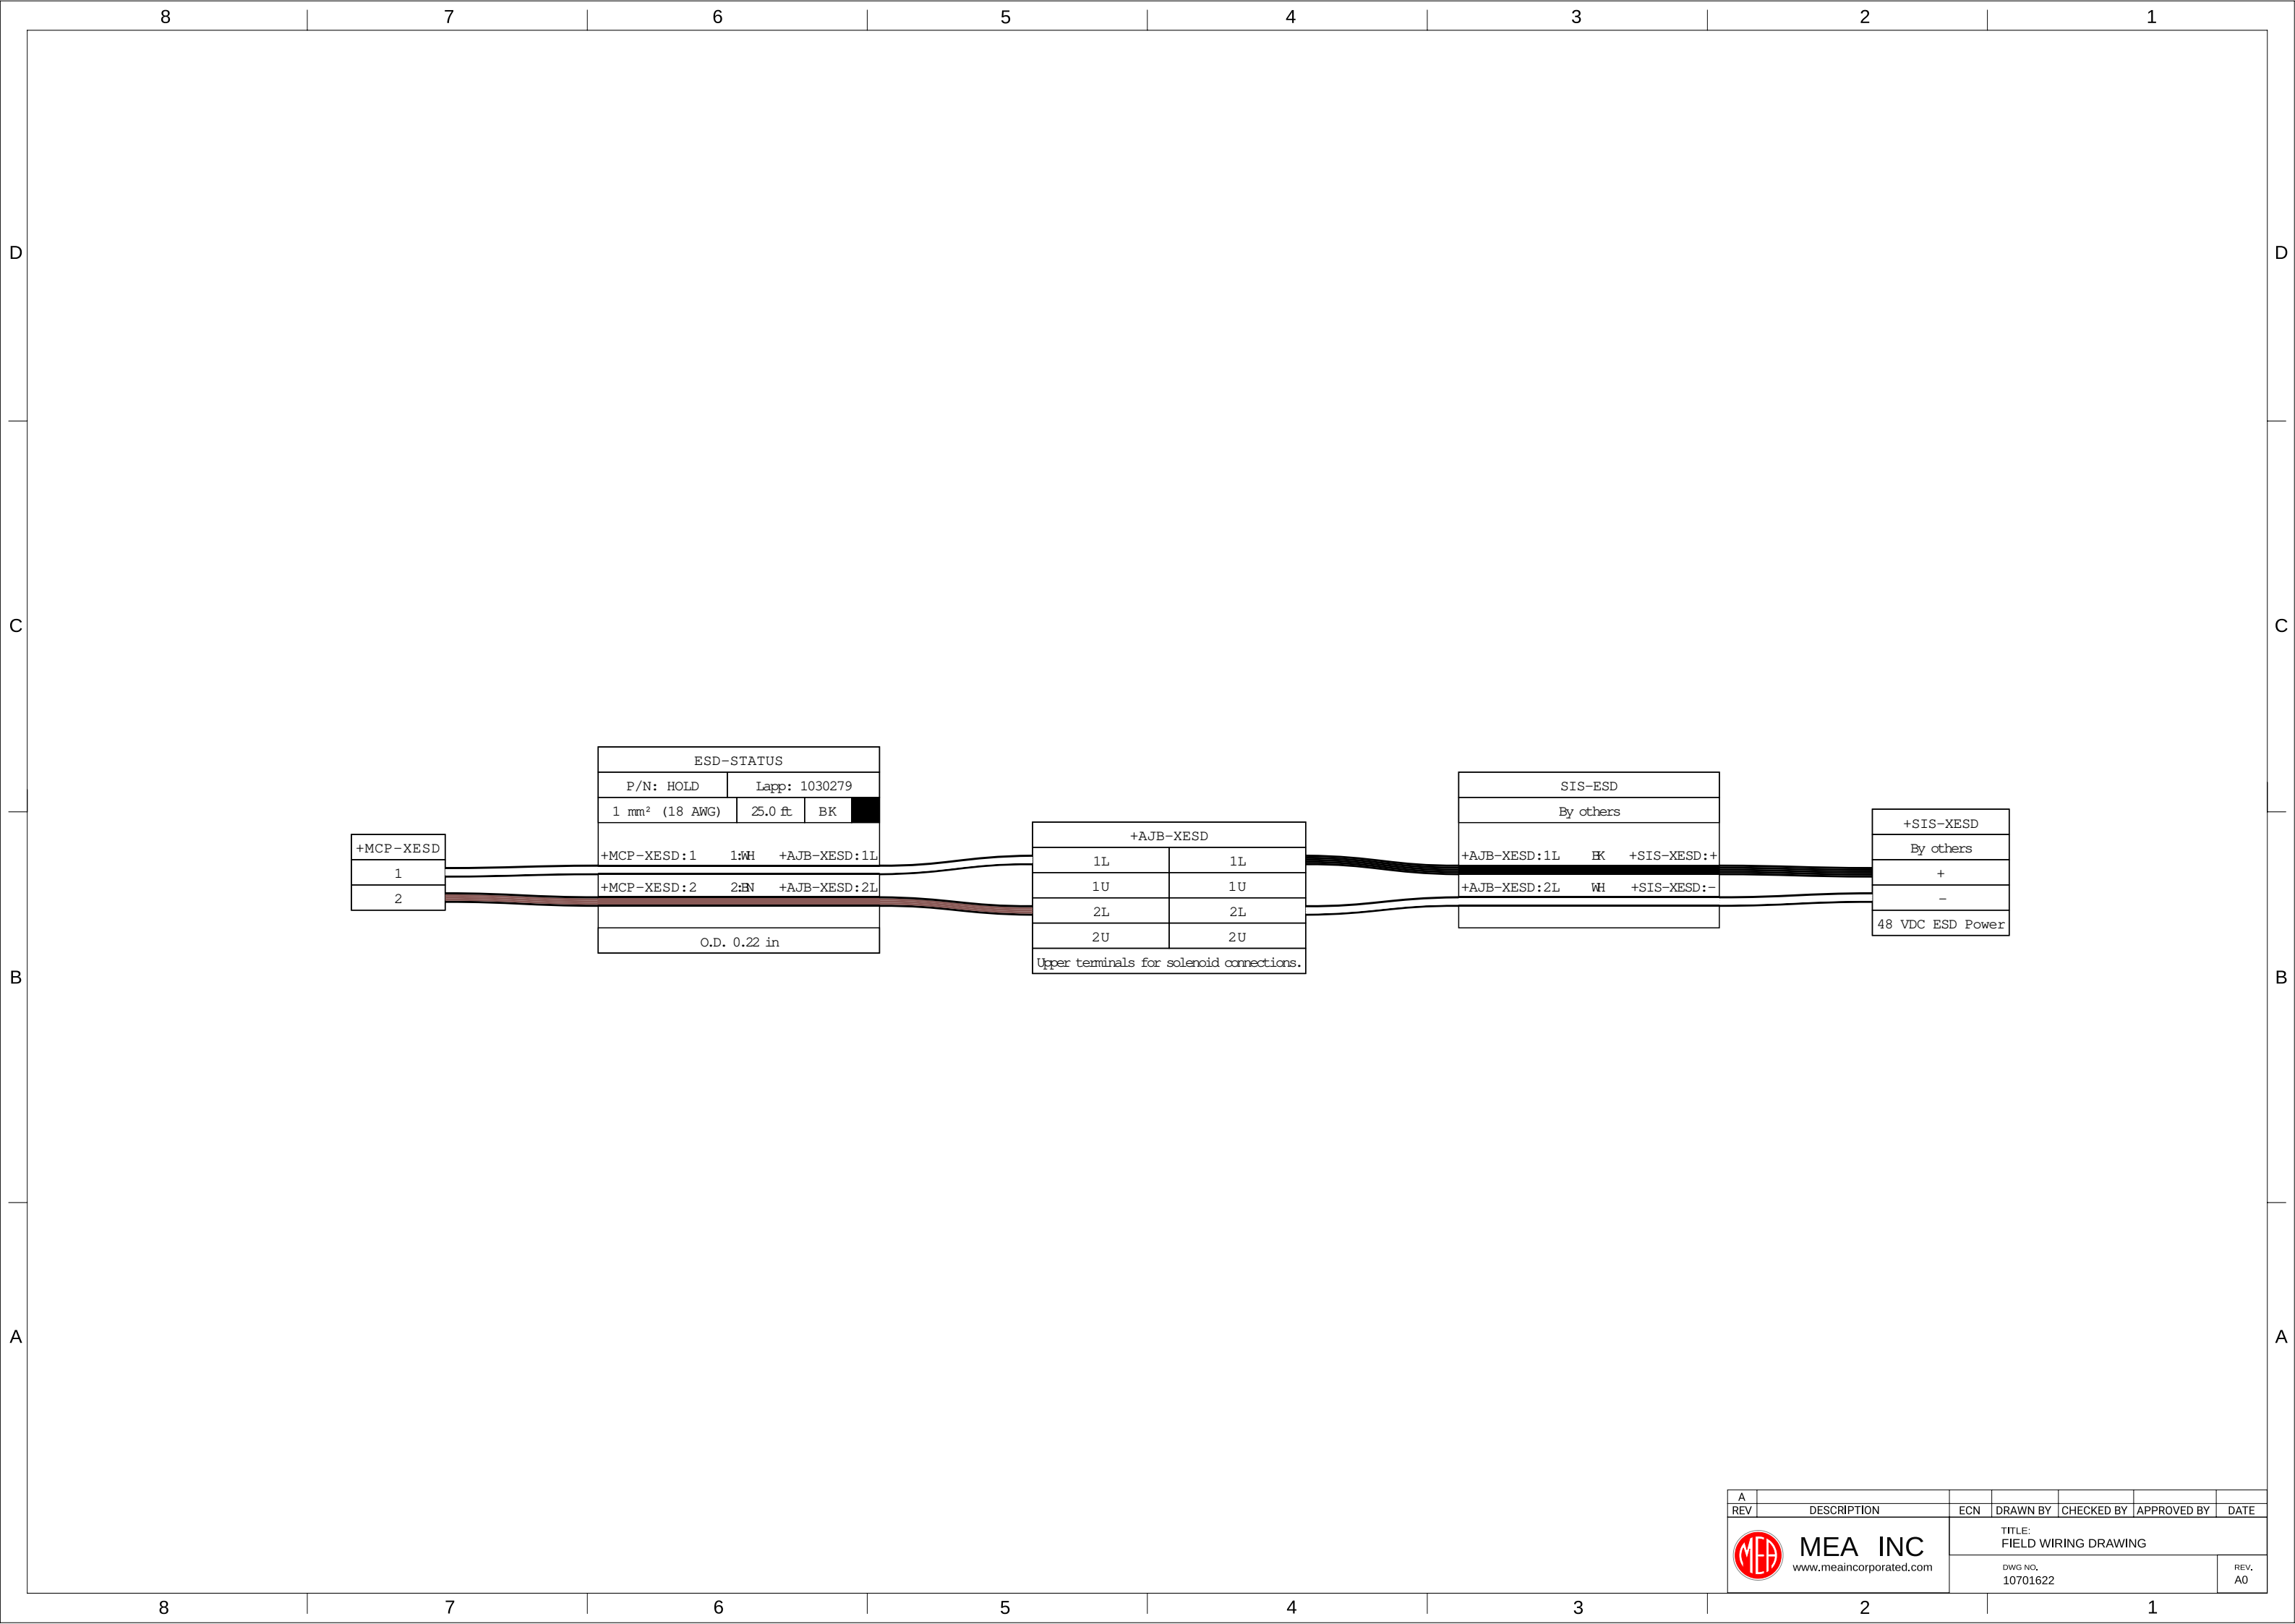

A						
REV	DESCRIPTION	ECN	DRAWN BY	CHECKED BY	APPROVED BY	DATE
 MEA INC www.meaincorporated.com		TITLE: FIELD WIRING DRAWING				
		DWG NO. 10701622				REV. A0

